

FILM FACILITATION CENTRE

SENTHIL VELAN S
311316251604
MEASI ACADEMY OF ARCHITECTURE

introduction 01

SCENARIO:

UPCOMING SOUND TECHNICIAN/ VFX ARTIST WANTS TO SET UP HIS STUDIO
CRITERIA FOR HIS SELECTION OF STUDIO SPACE

1. A "Go-to-place" where people know that there will be a Sound technician/ VFX Artist.
2. A place filled with Film industry people- Identifying niche market
3. Low cost rentable space OR at the center of the market with appropriate cost and investment.
4. Surrounded by other aspiring artists of the same field- This improves the chances of collaboration and promotes inter dependency.

SOLUTION:

One central hub where all of the above can be achieved – FILM FACILITATION CENTRE.



The center will have all the amenities and promote collaboration between aspiring artists/ technicians. Services offered for the following fields: Green Mat studio, VFX Studio, Editor's studio, Sound Mix Studio, Director's Office etc... (Appropriate fields to be added after further research)

FILM FACILITATION CENTRE

incubation centre for upcoming artist and technicians of film industry

STUDY PROCESS

USER/ CLIENT BASE

The project can be leased/ rented to artists of various fields upon completion, regardless of any union membership.

CLIENTS:

INDIE/ LOW BUDGET MOVIES | OTT PLATFORMS (Netflix, Amazon, Hotstar, Hulu..) | TELEVISION PROJECTS | TALKING HEADS/ INTERVIEWS CHANNELS | GATHERING CEREMONIES LIKE (AUDIO LAUNCH, SCREENINGS)

SCALE OF THE PROJECT:

Area of the Site, Number of Office/ Individual studio spaces.

SERVICES:

List of services- Description- Process Involved- Technical Details.

SPATIAL ANALYSIS:

Exploring the area and Material/ Structural considerations.

FUNCTION ANALYSIS:

Co Relation between different spaces.

PROJECT PALETTE:

Exploring Color, Texture, Experience.

SITE ANALYSIS:

Location relation to the success of the establishment.

HEAD QUARTERS WARNER BROS, LA Frank Gehry

Gehry Partners' plans for the 800,000-square-foot (74,000-square-metre) complex to extend the entertainment company's current building in the Burbank Media District. Located in the city of Burbank, the area has formed a hub for major media and entertainment companies such as Warner Bros since the 1920s.





WB HEADQUARTERS
"ICEBERG" DESIGNED BY FRANK GEHRY



FILM FACILITATION CENTRE

SENTHIL VELAN S
311316251604
MEASI ACADEMY OF ARCHITECTURE


studies & conclusions 02

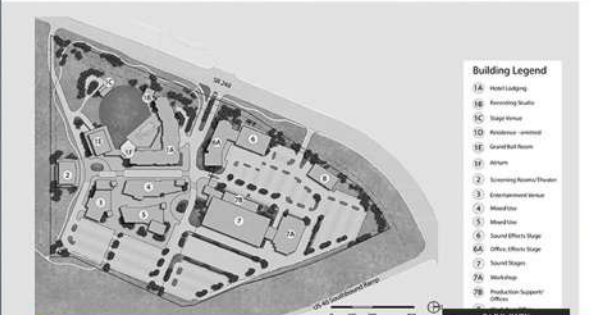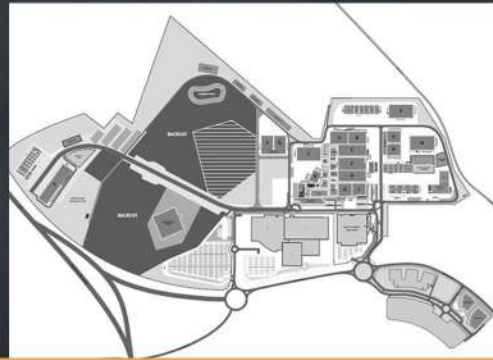

SCALE OF THE PROJECT

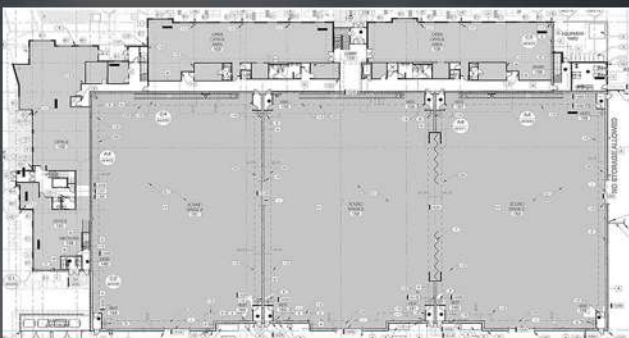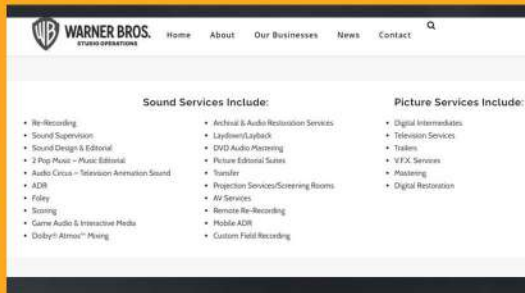

A Stage	
Dimensions	
Length	180m
Width	120m
Height	20m
Stage Size	33,400m²
Runway/Lifting Beams	
SWL - Load Between Trusses	1000k
SWL - Load Between Trusses	500kg
Stage Doors	
1 x Large dock door	18'0" x 18'0"
5 x Smaller doors	5.70m x 5.70m
Floor Type	
Concrete	
Electrical Supply	
Maximum electrical load: 1000kW (1000kW) / 1000kW (1000kW) / 1000kW (1000kW)	

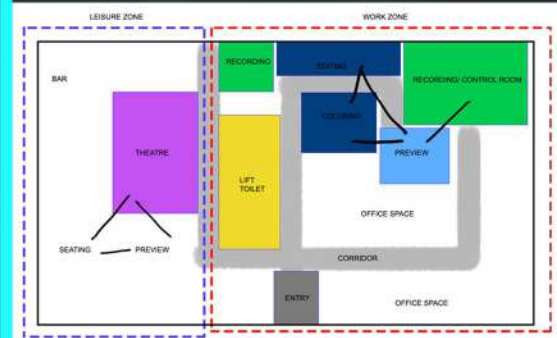


SPATIAL ANALYSIS & SERVICES



FUNCTION ANALYSIS



SITE ANALYSIS

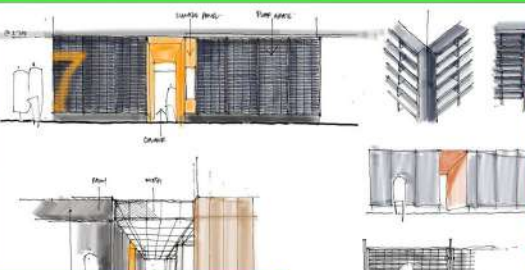

PALETTE- VISUAL AND SENSORY

FILM FACILITATION CENTRE

SENTHIL VELAN S
311316251604
MEASI ACADEMY OF ARCHITECTURE

site & basic design 03

Concept bubble explaining various services and their co relation to each other for maximum efficiency.

DERIVATION:

1. PRODUCTION WING

2. POST PRODUCTION WING

CHOOSING A SITE

Top Choices :


Vadapalani, ECR, Valasaravakkam

VADAPALANI




AVM Production House
Vishal Film Factory
Thirukumar Entertainment

Pins showing Established Film Production Houses (Excluding Individual Studios) in Vadapalani Area.

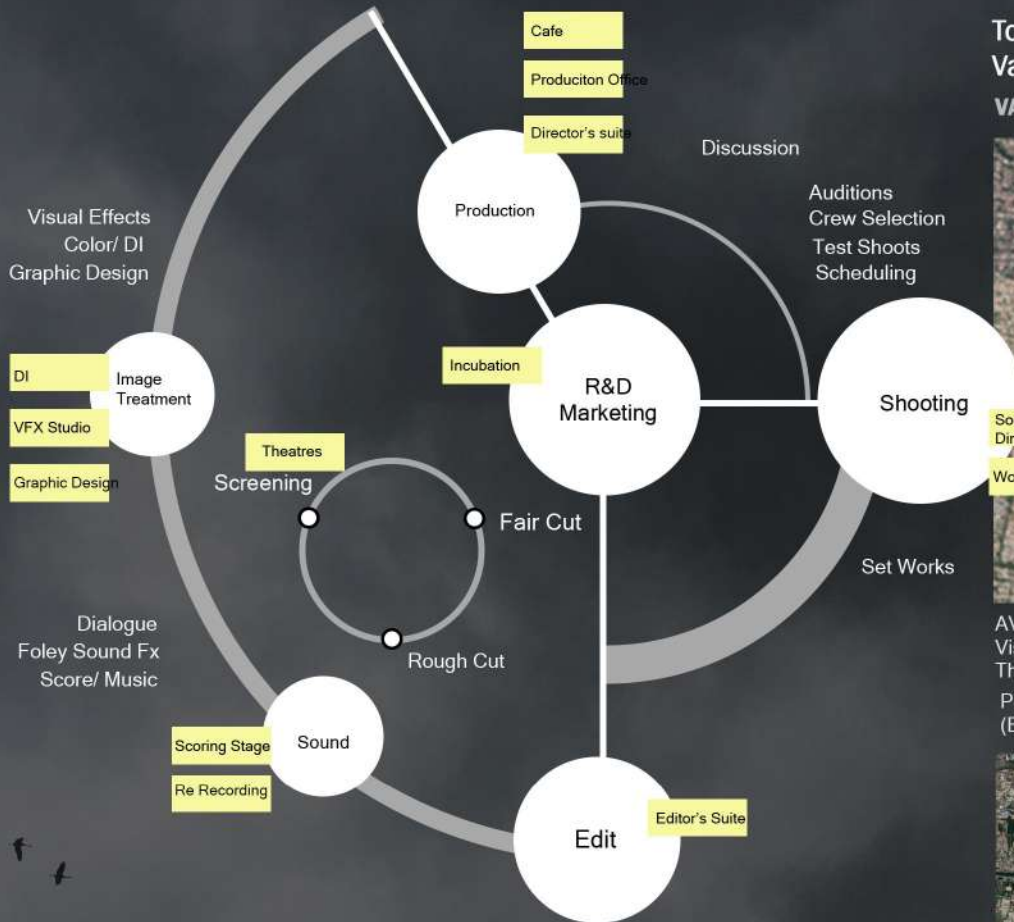


Services in the project derived from case studies and their relationship in production process

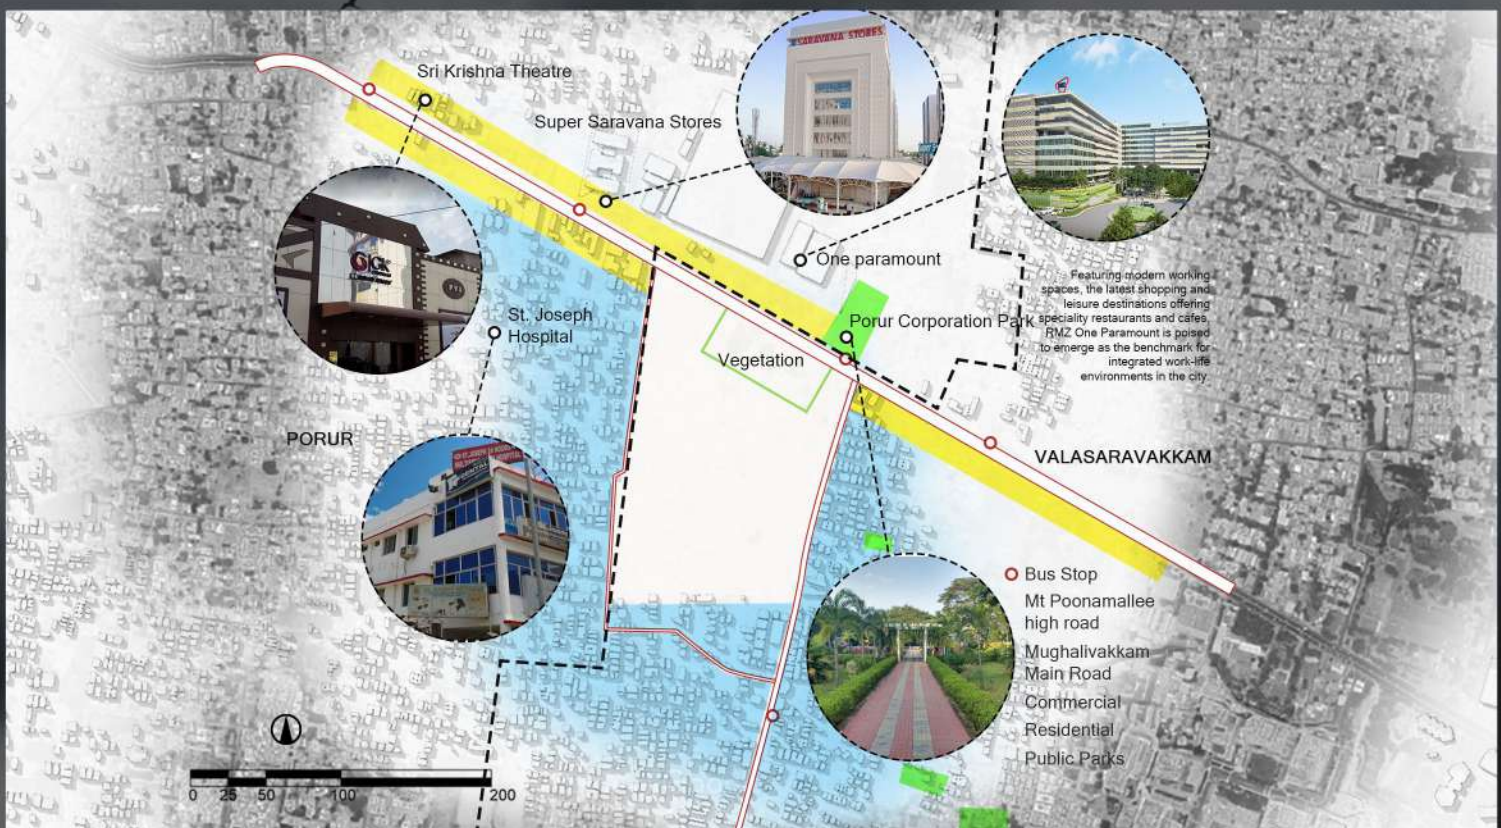

SENTHIL VELAN S
311316251604
MEASI ACADEMY OF ARCHITECTURE

SENTHIL VELAN S
311316251604
MEASI ACADEMY OF ARCHITECTURE

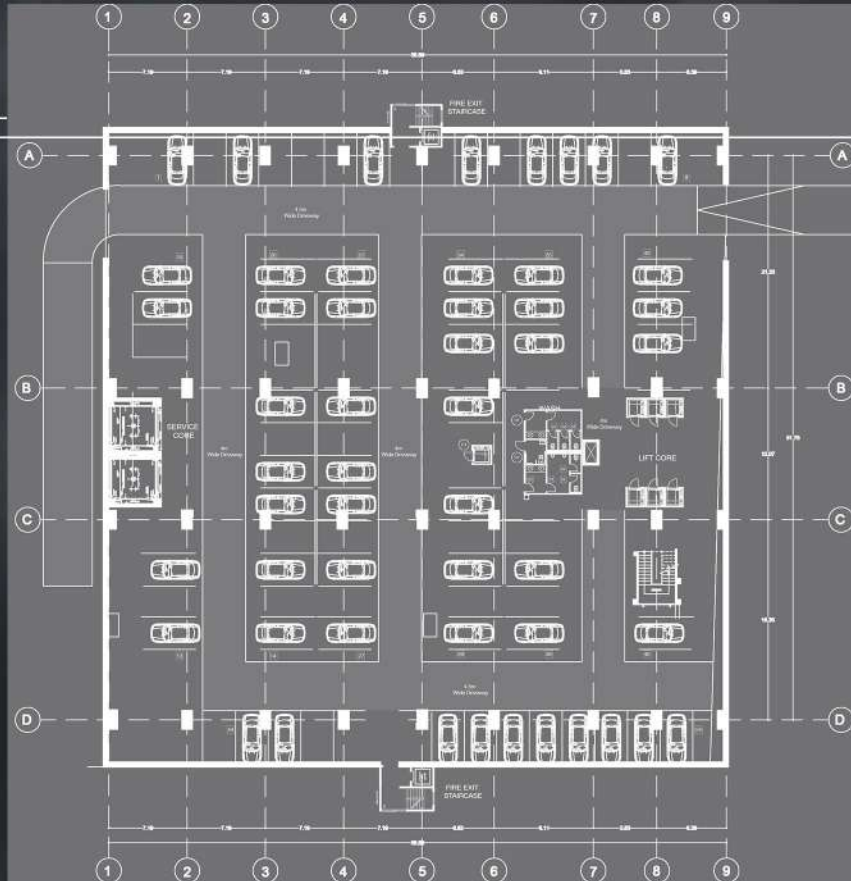

site plan 04


FILM FACILITATION CENTRE

SENTHIL VELAN S
311316251604
MEASI ACADEMY OF ARCHITECTURE

ground floor 05



Pavilion with Iridescent material

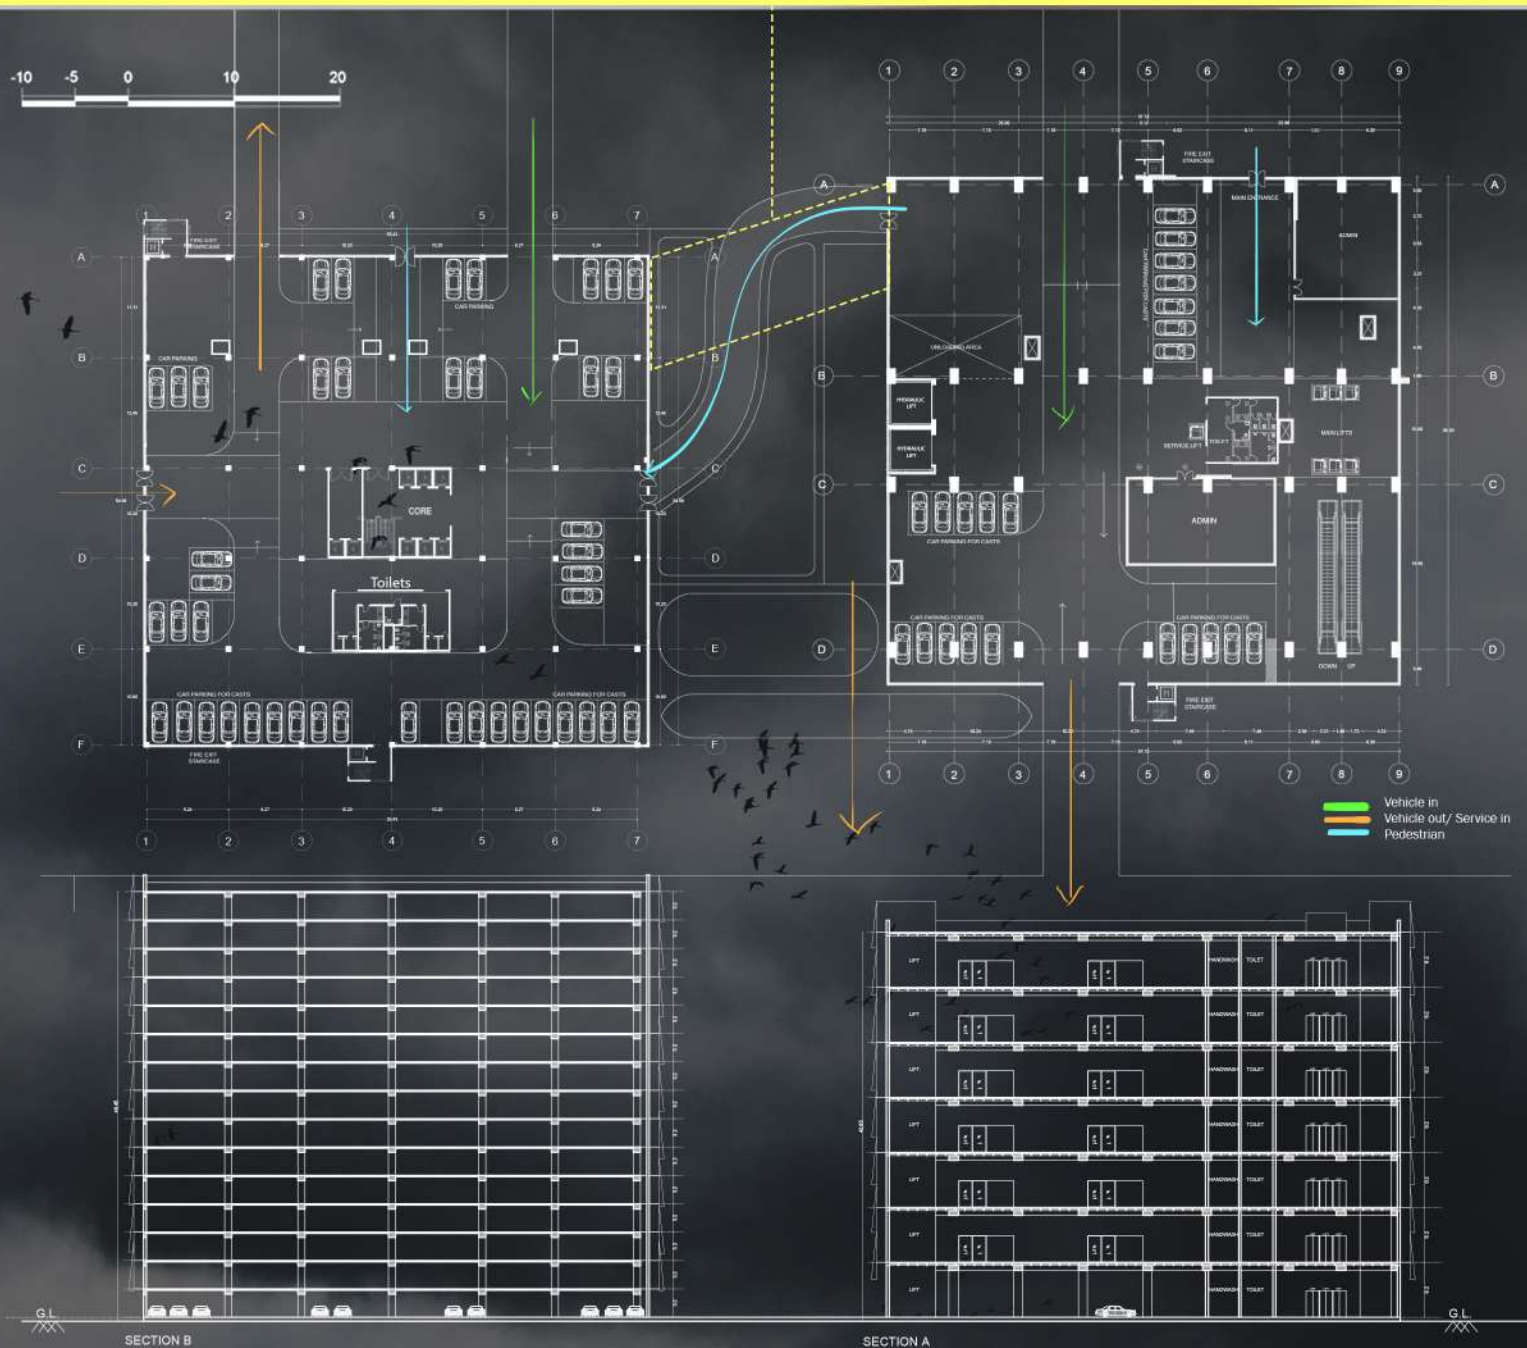


FILM FACILITATION CENTRE

SENTHIL VELAN S
311316251604
MEASI ACADEMY OF ARCHITECTURE

towe A typical **06**



8000 LBS. FREIGHT INGROUND HYDRAULIC
FRONT & REAR OPENING

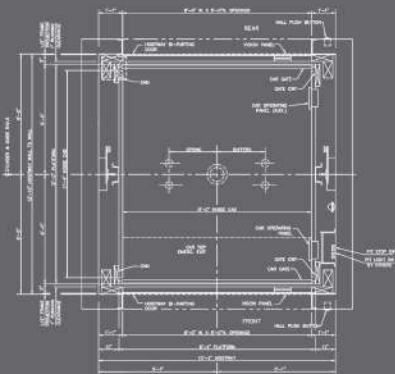

HOISTWAY PLAN
ALL DIMENSIONS ARE SUBJECT TO CHANGE WITHOUT NOTICE
CONTACT AUTOMATIC LIFTS CO. FOR COORDINATION
Nationwide Lifts
P: 888-692-4387, E: info@elevators.com

AREA

Sound Stage 1: 600 Sq m
Sound Stage 2: 200 Sq m
Dining : 200 Sq m
Workshop : 200 Sq m


FOOT FALL

Sound Stage 1: 100
Sound Stage 2: 50


Legend

D1 100 mm
D2 80 mm
DD 2000 mm
SD 6500 mm

10 5 3

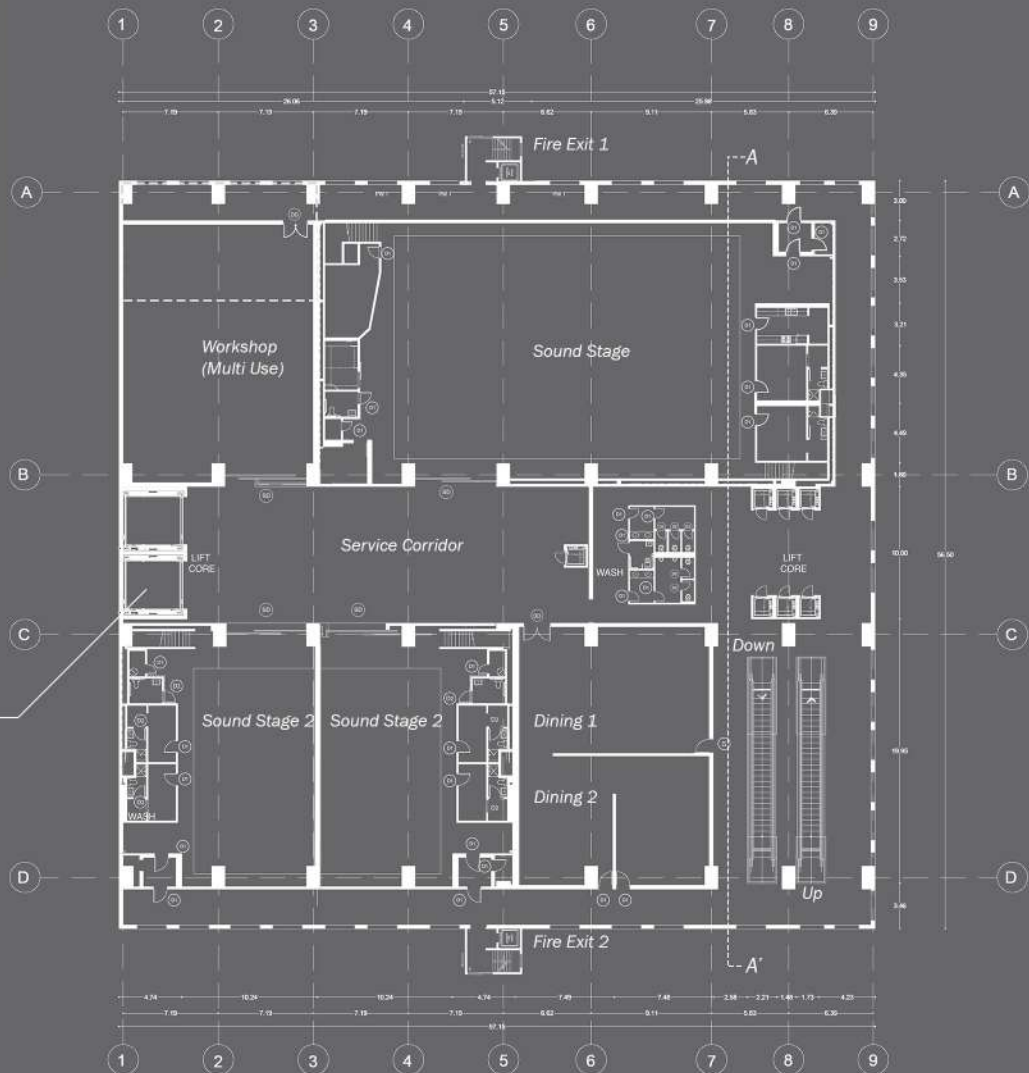

Tower A: Typical Plan

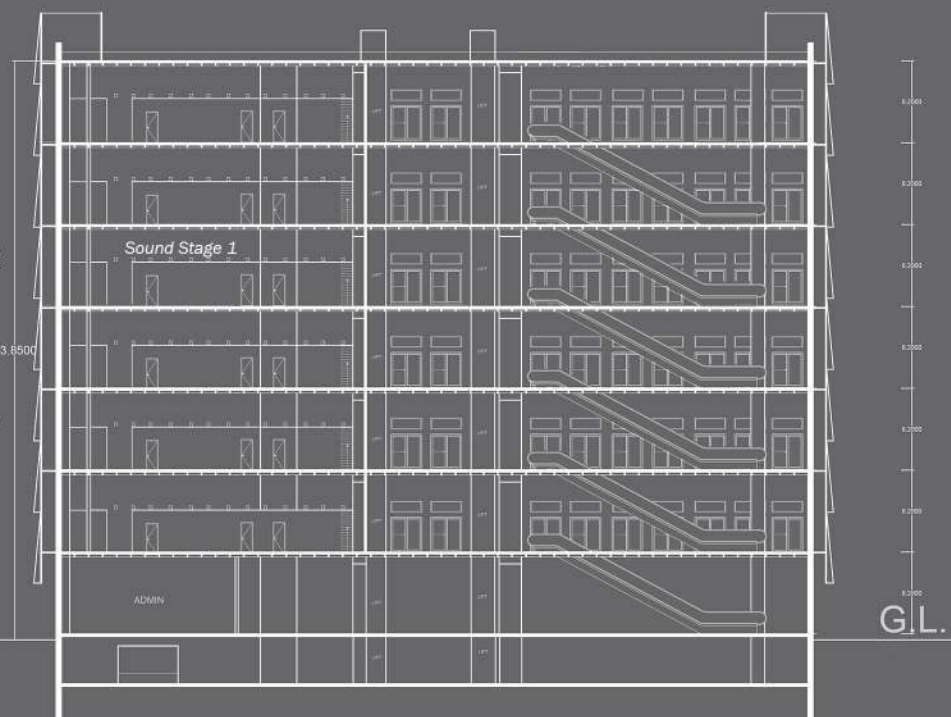

Section AA'

FILM FACILITATION CENTRE

SENTHIL VELAN S
311316251604
MEASI ACADEMY OF ARCHITECTURE

tower A sound stage 07



Video Village



Light Grid





Sound Proof section from
**Decent Air
System pvt Ltd.**

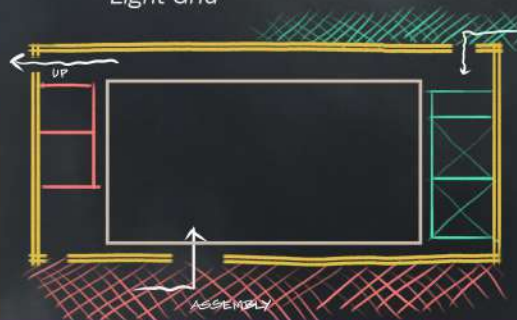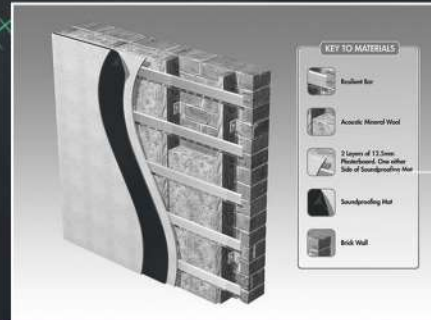

Dolly
Heavy Equipments

Typical Sound stage
Layout

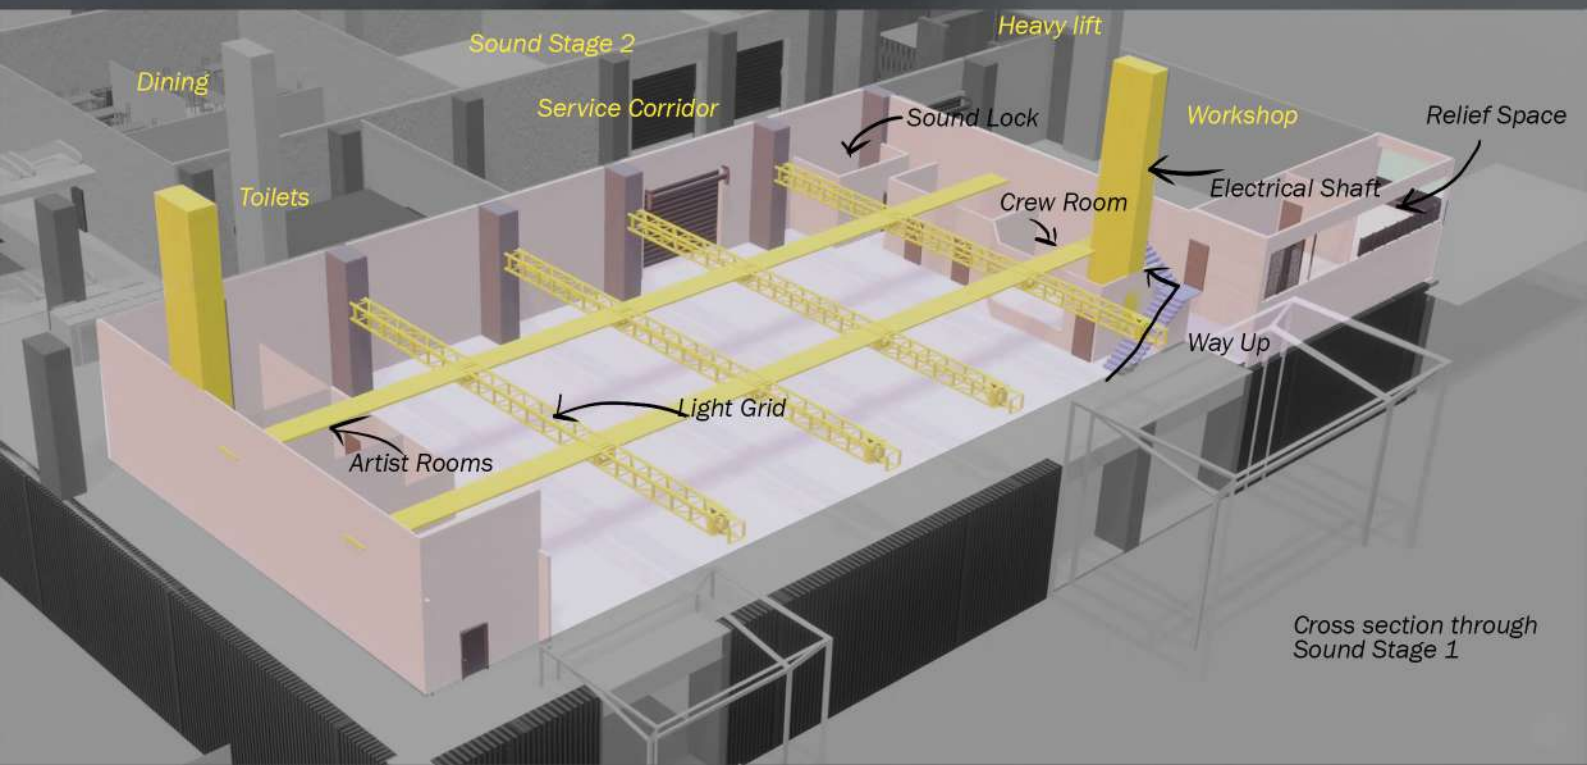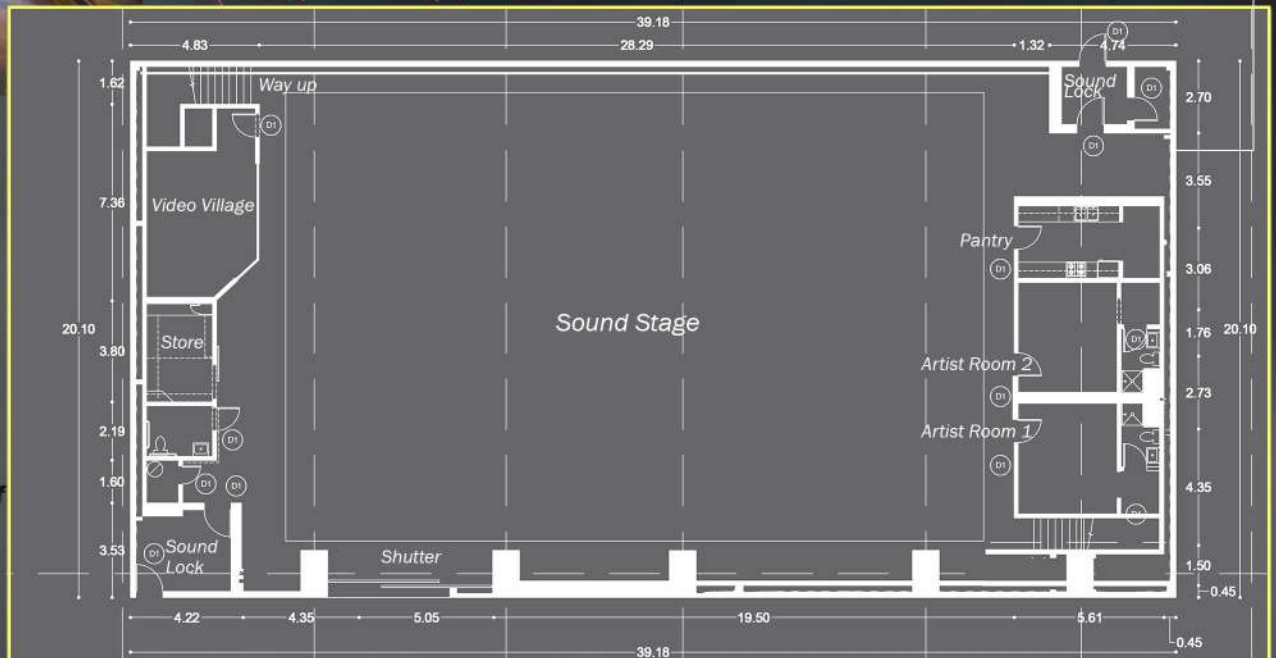


Cross section through
Sound Stage 1

FILM
FACILITATION
CENTRE


SENTHIL VELAN S
311316251604
MEASI ACADEMY OF ARCHITECTURE

tower B typical 08


THREE TYPICAL FLOOR PLANS IN TOWER B

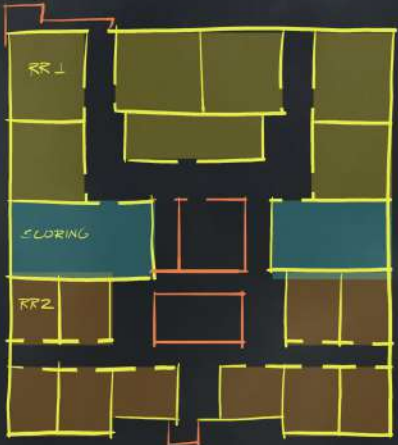

Sound Floor

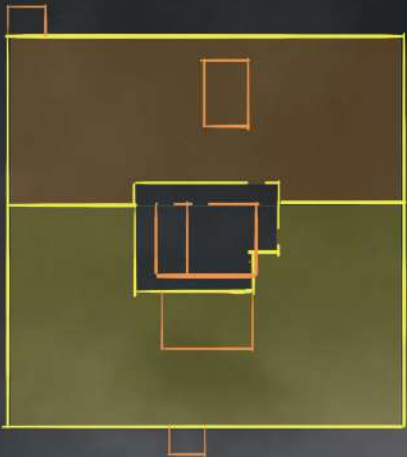

Indie Floor

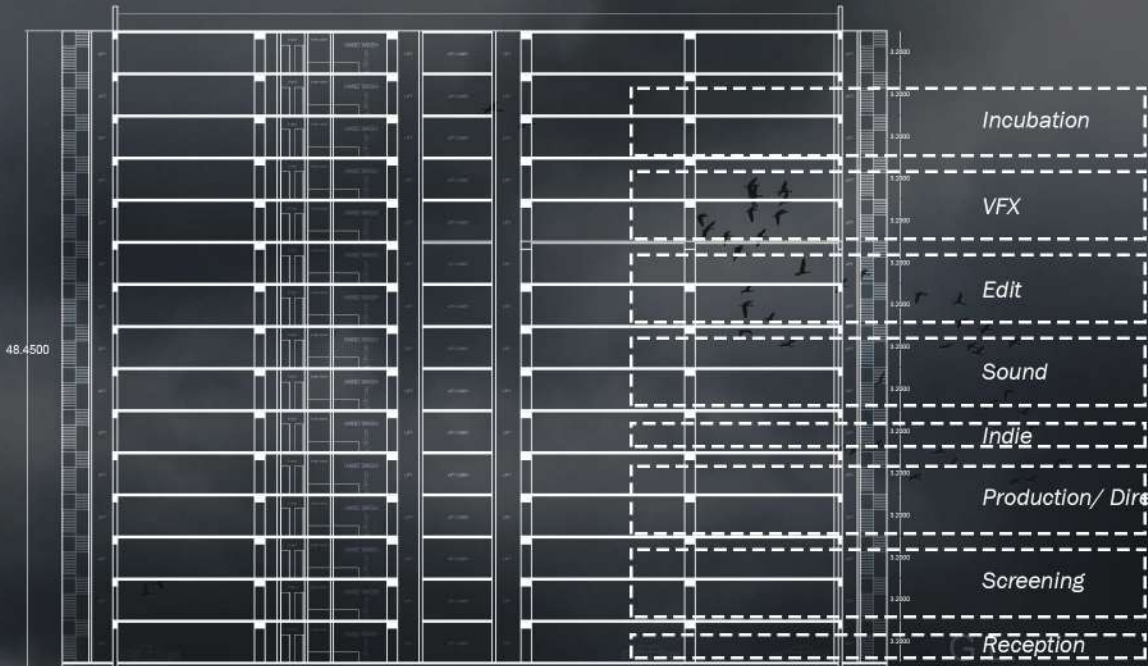


Area statement

STUDIOS	TYPE 1	TYPE 2
Editor	150	80
Re recording	150	80
Render Farm	80	
Scoring	200	
DI	80	
VFX tudio	100	
Graphic Design	100	
Poduction Office	100	
Marketing Office	200	100
Theatre	100	
Screening Room	300	

FILM FACILITATION CENTRE

SENTHIL VELAN S
311316251604
MEASI ACADEMY OF ARCHITECTURE





UNIT TYPE 1

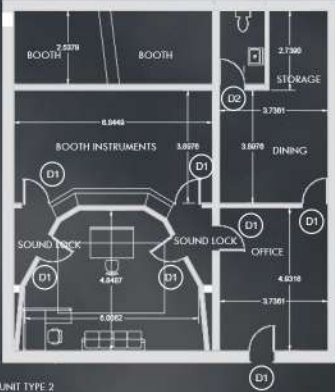

UNIT TYPE 2



Sound:
Re recording
Scoring

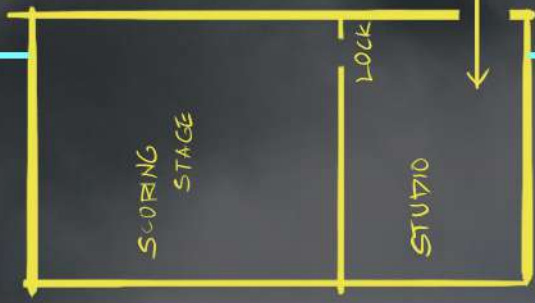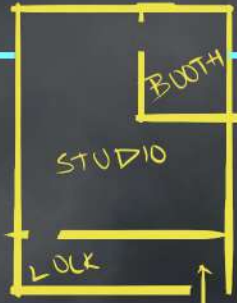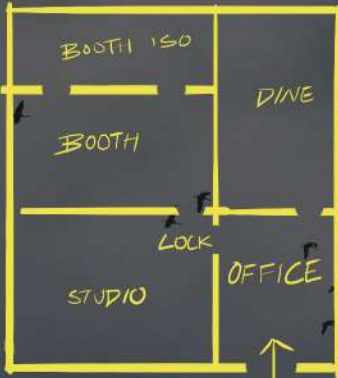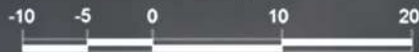

tower B floorplans 09




North View from
Poonamallee High Road


FILM FACILITATION CENTRE

SENTHIL VELAN S
311316251604
MEASI ACADEMY OF ARCHITECTURE

tower B floorplans 10

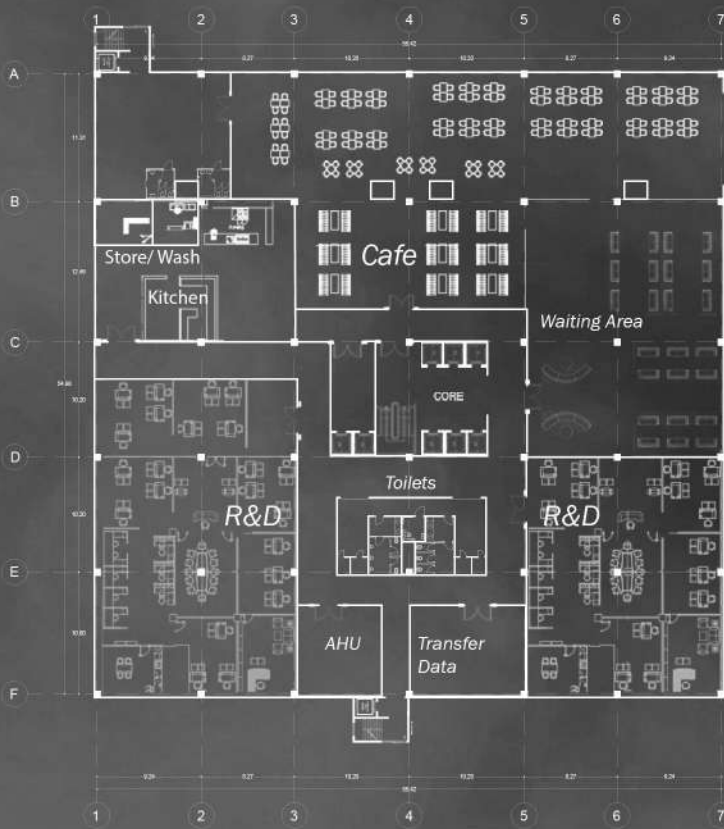

Cafe/ R&D

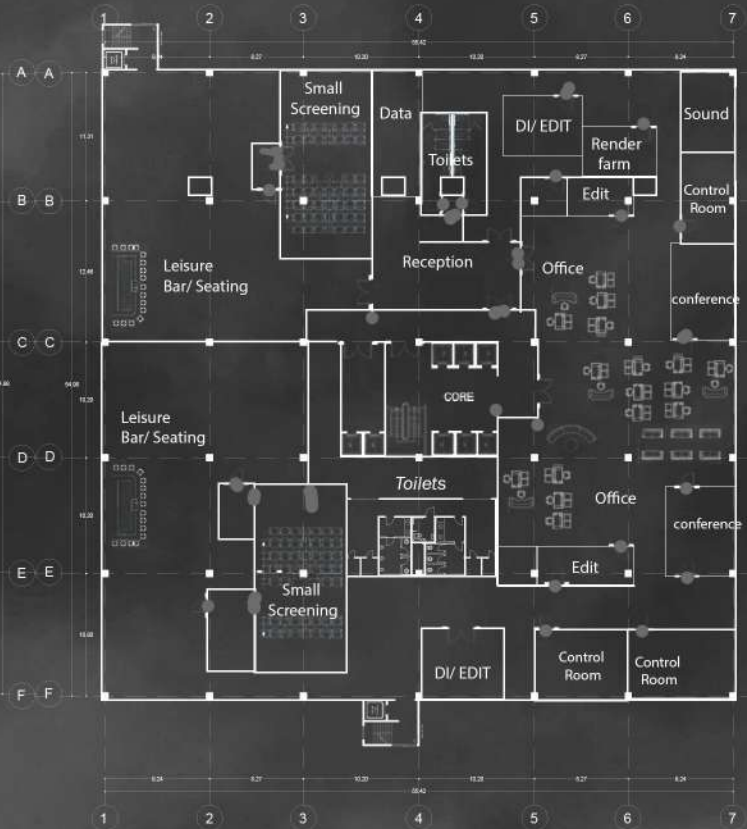

Indie Production House



*North West View from
Poonamallee High Road*



FILM FACILITATION CENTRE

SENTHIL VELAN S
311316251604
MEASI ACADEMY OF ARCHITECTURE

tower B floorplans 11



View from Service Entry
Mugalivakkam Main Road




FILM FACILITATION CENTRE

SENTHIL VELAN S
311316251604
MEASI ACADEMY OF ARCHITECTURE

kinetic structures 12

Terrace

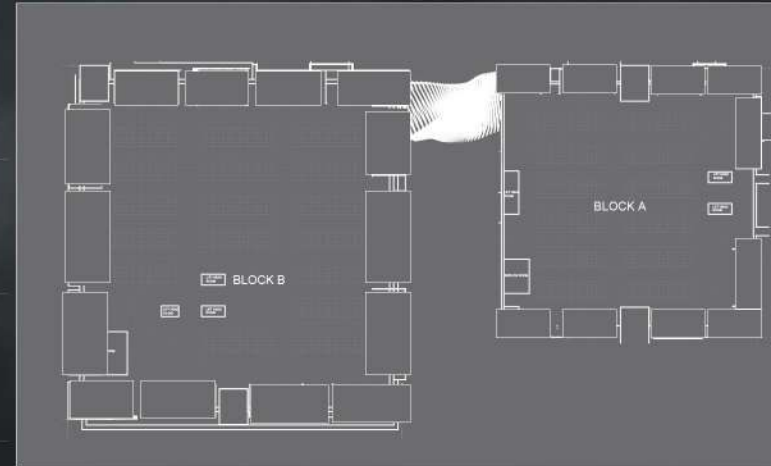

PHILOSOPHY

MOVIE: Dynamic images

Achieving Dynamics through FORM using Kinetic Facades that can adjust to sun Direction accounting to optimum heat gain of the building block.

Wall Window



6.2 m (One floor height in Tower A
Two floor height in Tower B)

Frame work holding the
Facade at its Centre of Gravity

Kinetic Facade Section

Kinetic Facade:


These facades may be operated both manually and automatically according to the need.



FILM FACILITATION CENTRE

SENTHIL VELAN S
311316251604
MEASI ACADEMY OF ARCHITECTURE


palette 13

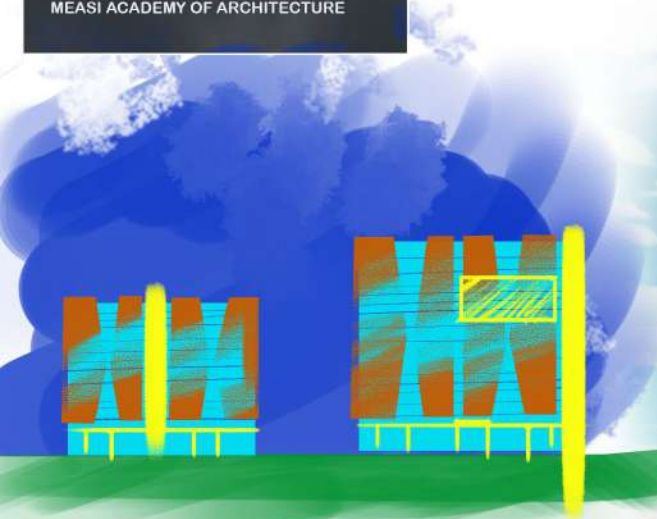


Achieving Dynamics in Materials




Iridescence: Peacock Feather

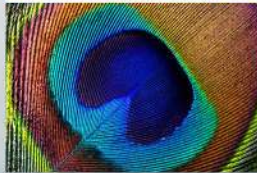


Using the colors in Peacock Feather as the Palette

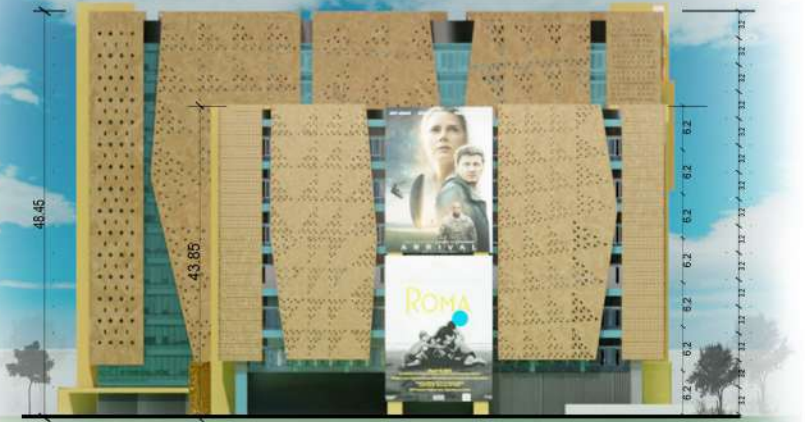

East Elevation

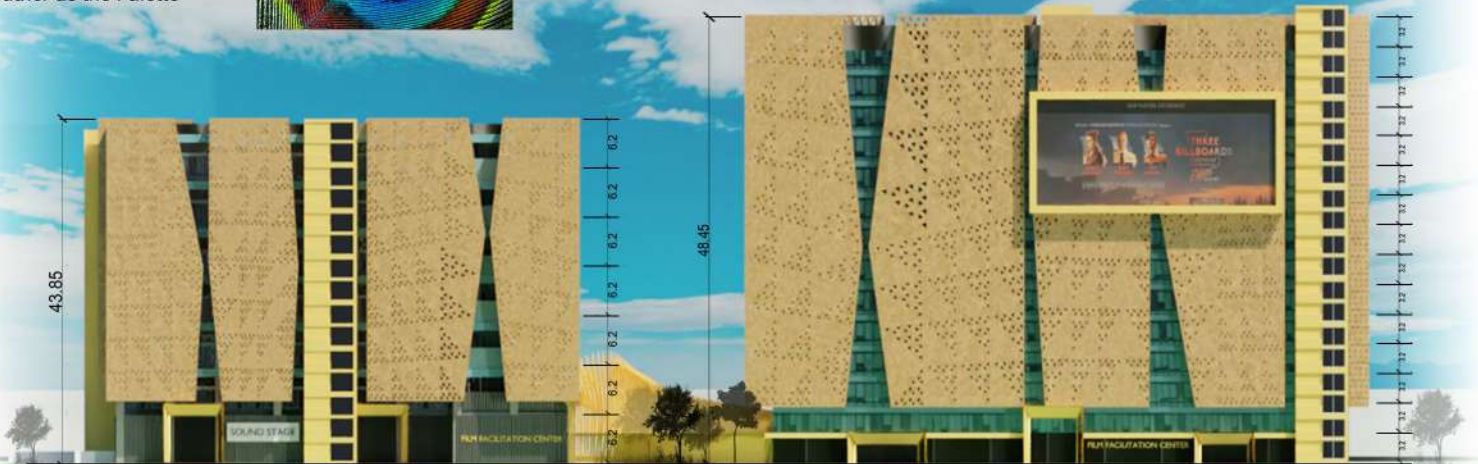

North Elevation

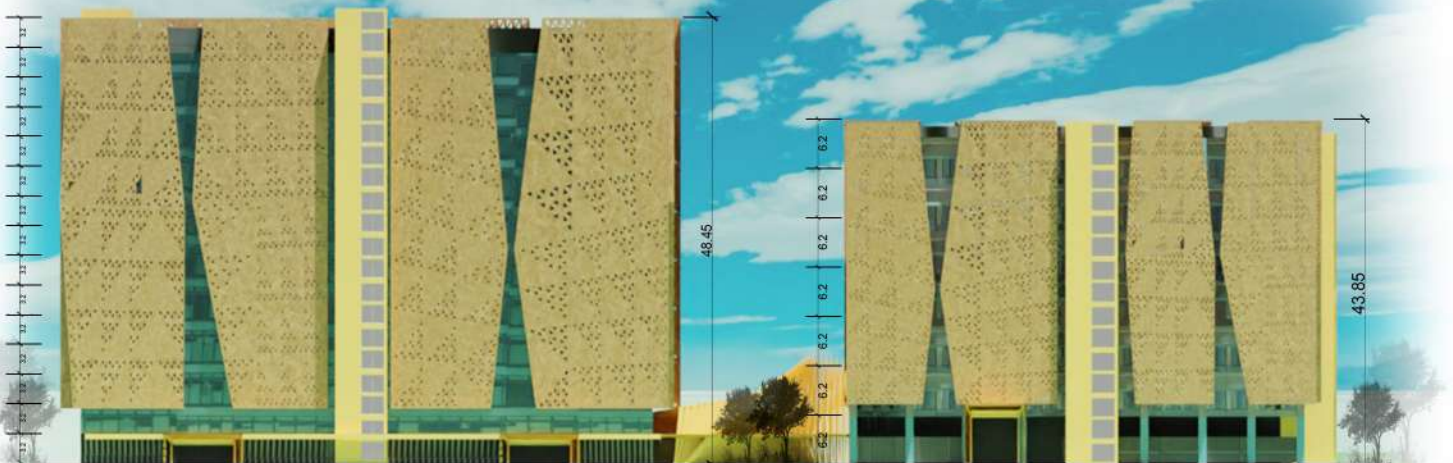

South Elevation